

GS EXTERIOR EXPERTS · DECK DIVISION · PERMIT SET

16 x 14 Deck · Permit Set

16' x 14' · 2'-4" high · ledger to the house · 2x10 SYP @ 16" · 4x10 DF beam
on 4 Diamond Piers · Prime+ Sea Salt Gray, single picture frame · Fulton black
· 5' stair to the existing pad · September 30, 2026

SHEET INDEX

- | | |
|--|--|
| 1. 16 x 14 deck · G-001 General notes · design criteria | 5. 16 x 14 deck · A-201 Railing plan + elevation |
| 2. 16 x 14 deck · S-100 Foundation plan | 6. 16 x 14 deck · A-301 Section + front elevation |
| 3. 16 x 14 deck · S-101 Framing plan | 7. 16 x 14 deck · D-501 Details |
| 4. 16 x 14 deck · A-101 Decking plan | |

Design intent. The stamped engineering set governs structure, dimensions and locations. Field verify. Do not scale. This set carries no pricing.

16 x 14 deck · G-001 · General notes · design criteria

G-001 GENERAL NOTES · DESIGN CRITERIA		16 x 14 Deck — TimberTech Prime+ Sea Salt Gray, Fulton rail	
Loads, codes, structure summary, sheet index, site — the permit-set cover		GSX · Jade Pender 303-550-9558 · September 30, 2026 · Rev 0 · PERMIT SET	
PROJECT		SHEET INDEX	
16 x 14 Deck — TimberTech Prime+ Sea Salt Gray, Fulton rail		G-001	General notes · design criteria
CO		A-001	Isometric · renders
220 SF · 2'-4" above grade · 1 zone		S-100	Foundation plan
DESIGN CRITERIA		S-101	Framing plan
Deck live load	40 psf uniform (IRC Table R301.5); guards 200 lb concentrated / 50 plf	A-101	Decking plan
Ground snow	30 psf (ground; deck design uses the larger of snow and live) — 40 psf live governs	A-201	Railing plan + elevation
Dead load	10 psf deck	A-301	Section + front elevation
Roof snow (cover)	—	D-501	Details
Design total	50 psf on the deck	SITE	
Wind	115 mph Vult, Exposure C, Risk Cat. II (ASCE 7-16) — confirm special wind region	Setbacks not on file — verify the plat / ILC before layout	
Frost depth	3'-0" (footings bear below)		
Soil bearing	1,500 psf presumptive (IRC R401.4.1) — no soils report		
Seismic	B		
Wildfire (WUI)	not in a WUI zone		
Codes	2021 IRC as adopted by the jurisdiction; IRC R507 decks; ASCE 7-16 loads; Tables R507.5 / R507.6 / R507.4 / R507.9		
Engineering	Prescriptive; no engineering required by this design		
STRUCTURE			
Footings	DP-50/50		
Posts	4 x 6x6		
Beams	DROP 4x10 DF: 15'-8", 4 posts at 1'-0 1/2" / 5'-7 3/16" / 10'-1 13/16" / 14'-8 1/2" (worst 1,796 lb)		
Joists	13 2x10 #1 True Frame Joist SYP GC @ 16" OC x 13'-4 1/2"		
Rims	2-ply 2x10 front and sides		
Ledger	2x10 ledger x 15'-9" total · LedgerLOK 2 rows 2" from top/bottom, staggered 12" OC, first 3" from each end · 17 fasteners		
Decking	TimberTech Prime+ Sea Salt Gray — 29 rows parallel to the house, picture frame in Prime+ Sea Salt Gray, 3/16" gaps, Camo EdgeClip		
Rail	Fulton 36" Black: 6 bays, 8 posts, 38 LF		
No scale		Design intent per 2021 IRC R507 prescriptive. Field verify. Do not scale.	

16 x 14 deck · S-100 · Foundation plan


S-100

FOUNDATION PLAN

Footings, posts and beam lines with the footing schedule; beams dashed (below the joists)

16 x 14 Deck — TimberTech Prime+ Sea Salt Gray, Fulton rail

GSX · Jade Pender 303-550-9558 · September 30, 2026 · Rev 0 · PERMIT SET

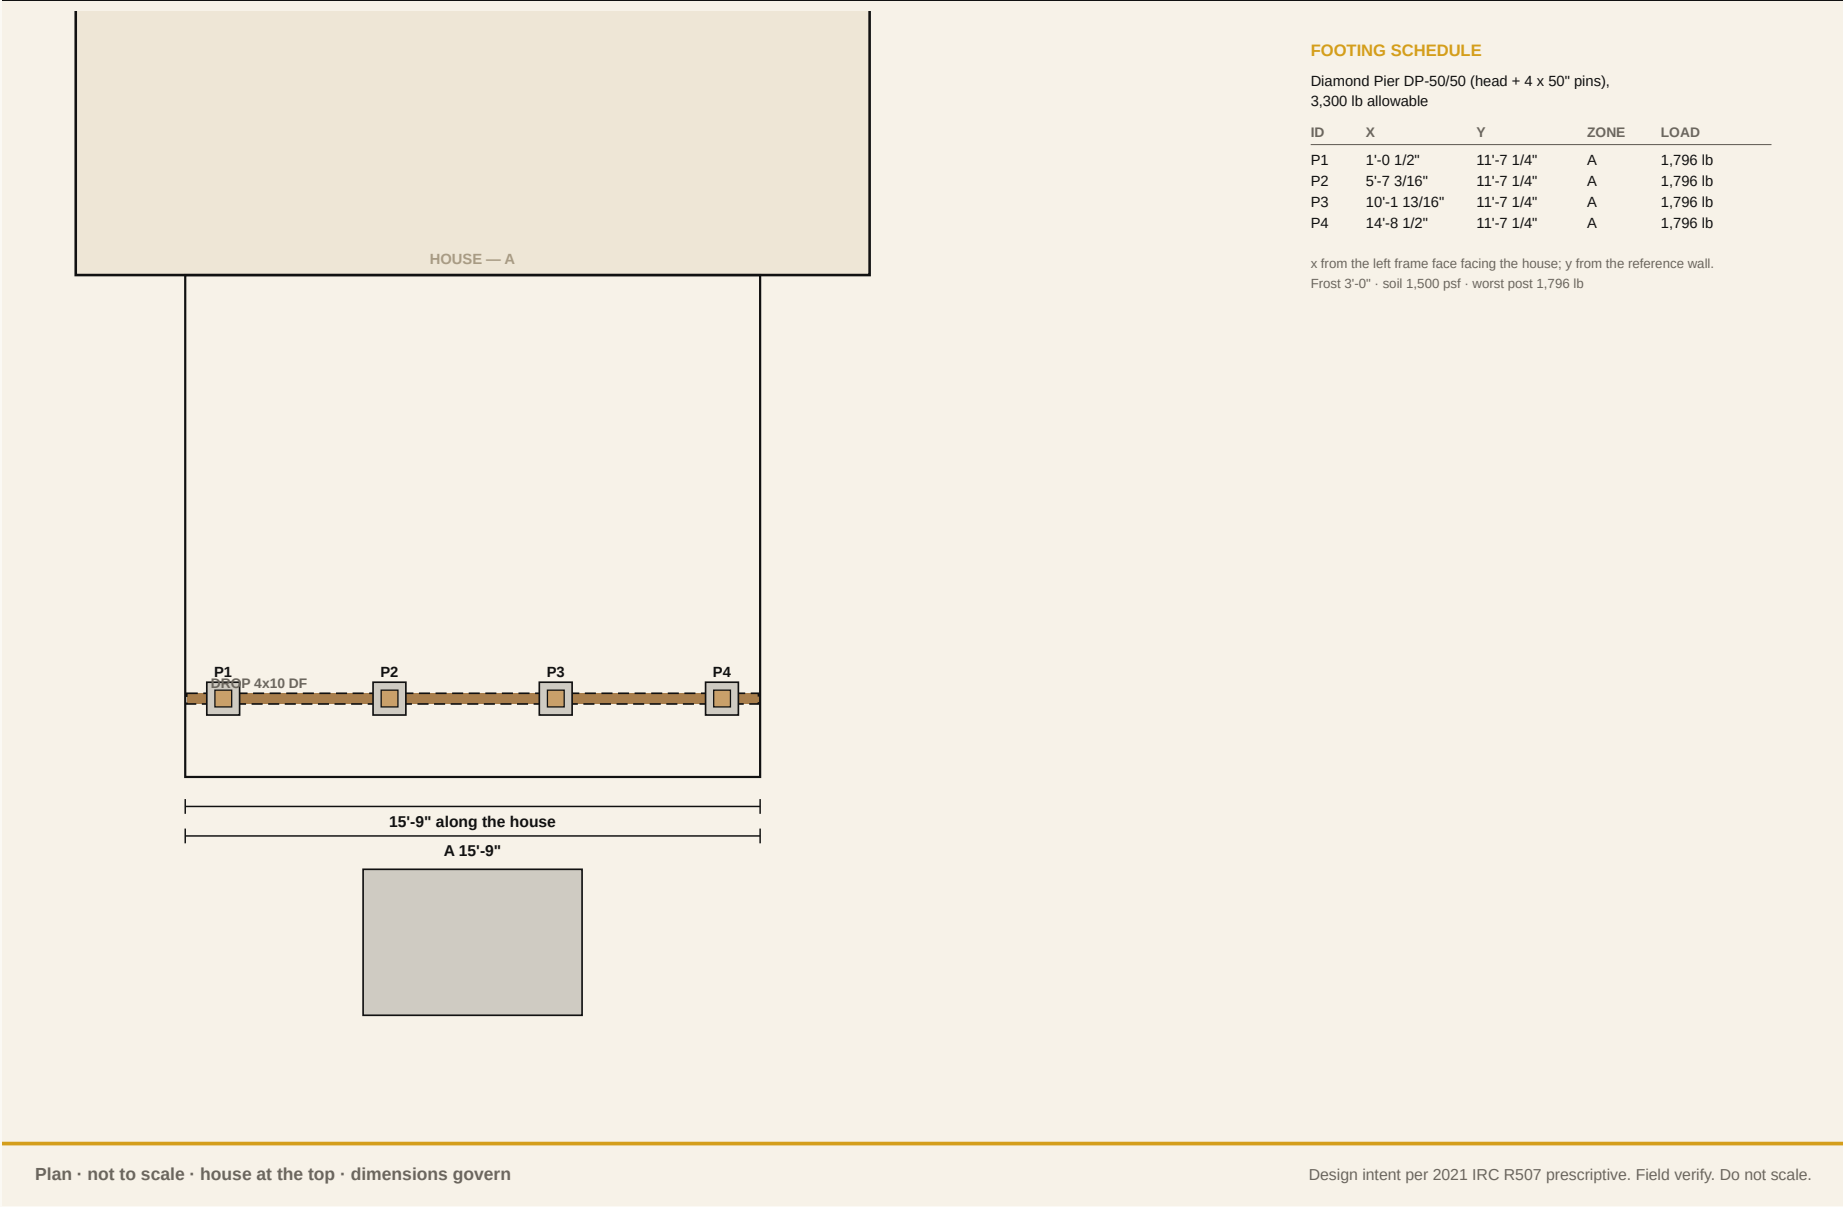

16 x 14 deck · S-101 · Framing plan


S-101

FRAMING PLAN

Ledger, joists, rims, blocking, beams; every member in the model — the cut list is on T-600

16 x 14 Deck — TimberTech Prime+ Sea Salt Gray, Fulton rail

GSX · Jade Pender 303-550-9558 · September 30, 2026 · Rev 0 · PERMIT SET

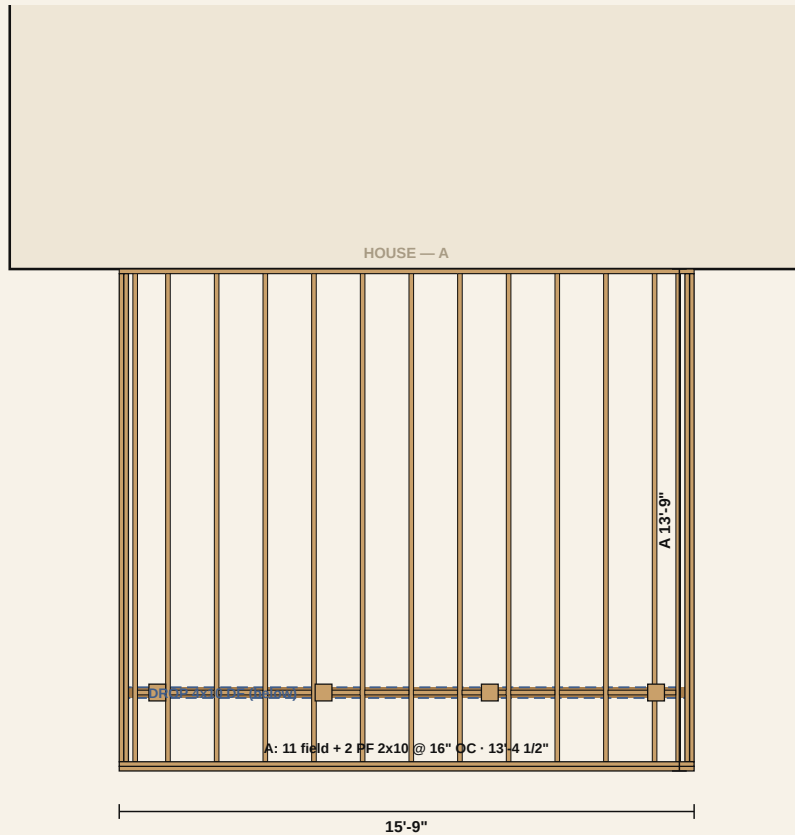

FRAMING NOTES

13 2x10 #1 True Frame Joist SYP GC @ 16"
OC x 13'-4 1/2"

2-ply 2x10 front and sides

2x10 ledger x 15'-9" total · LedgerLOK 2
rows 2" from top/bottom, staggered 12"
OC, first 3" from each end · 17

blocking one row over the beam,
staggered

G-Tape 2" every joist, PF joist,
blocking and the ledger top · 4" on both
rims and the beam(s)

DROP 4x10 DF: 15'-8", 4 posts at 1'-0
1/2" / 5'-7 3/16" / 10'-1 13/16" / 14'-8
1/2" (worst 1,796 lb)

Connectors:

Simpson LUS28Z face-mount hanger
2x8/2x10: 26

Simpson HUCQ210-2-SDS concealed-flange
double 2x10 hanger (SDS screws
included): 4

Simpson DTT1Z lateral tie kit w/ SDS
screws: 4

Simpson H2.5AZ hurricane tie (joists to
the drop beam, hidden): 15

Simpson BC46Z post cap 6x post / 4x
beam: 4

7/16" x 4-1/2" HDG hex bolt + nut + 2
washers: 24

Simpson LSCZ adjustable stair-stringer
connector: 6

16 x 14 deck · A-101 · Decking plan

A-101

DECKING PLAN

Every board, border and divider as it lays; rail posts shown for the pockets

16 x 14 Deck — TimberTech Prime+ Sea Salt Gray, Fulton rail

GSX · Jade Pender 303-550-9558 · September 30, 2026 · Rev 0 · PERMIT SET

DECKING

Field: TimberTech Prime+ Sea Salt Gray,
5.36" x 0.94", 3/16" gaps


Border: Prime+ Sea Salt Gray

Boards run parallel to the house; edge
overhang 1 1/16" over the fascia

100% hidden — Camo EdgeClip 3/16" at
every joist in every gap (13 bearing
points x 29 gaps = 377); board ends
clipped on the PF joists, never screwed

Cap-Tor xd color-matched ONLY at: first
row 1 per joist on the house edge ·
borders 2 per bearing point @ 16" ·
fascia 2 at each board end then

Rows per zone: A 29 (no rips)

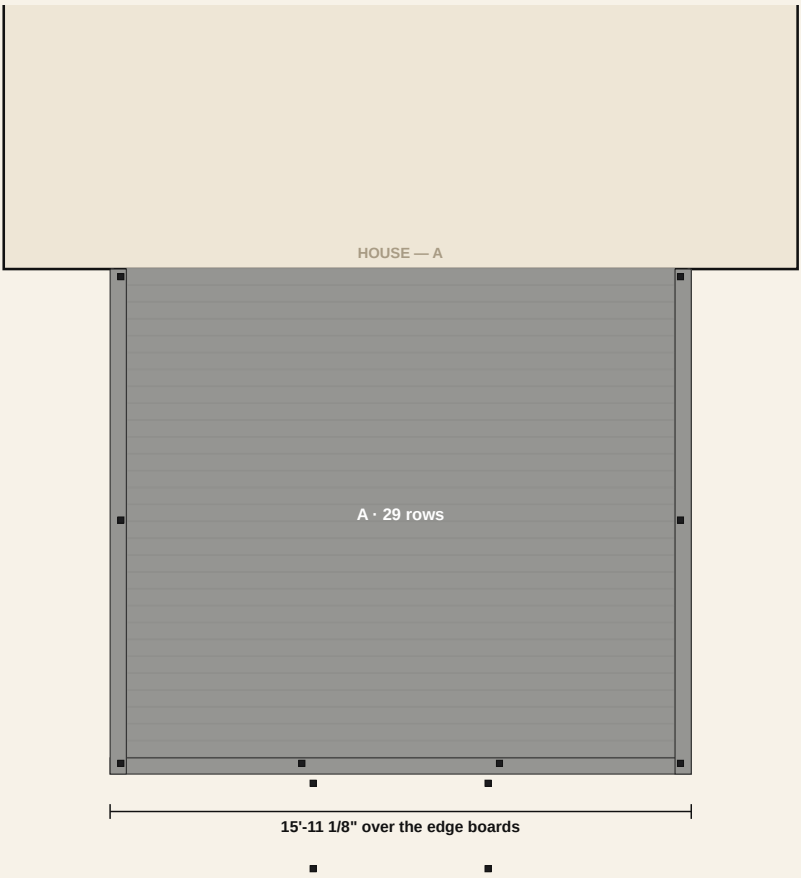

16 x 14 deck · A-201 · Railing plan + elevation


A-201

RAILING PLAN + ELEVATION

Post IDs and types (E end · L line · C corner), bay lengths, outer-edge elevation


16 x 14 Deck — TimberTech Prime+ Sea Salt Gray, Fulton rail

GSX · Jade Pender 303-550-9558 · September 30, 2026 · Rev 0 · PERMIT SET

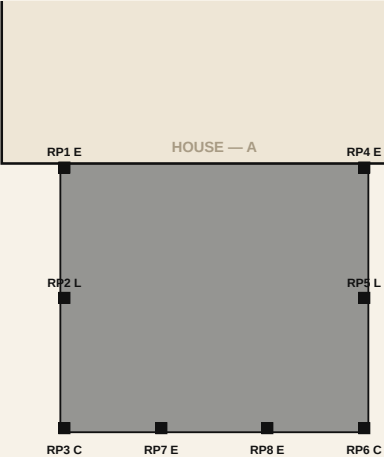

RAILING

Fulton 36" Black: 6 bays, 8 posts, 38 LF
Fulton 36" — 8 posts (2 CORNER, 4 END, 2 LINE) inside the outer rim ply, inner ply pocketed 2" wide, (2) 7/16" x 4-1/2" bolts per post
Bays: left 6'-8" · left 6'-8" · right 6'-8" · right 6'-8" · front 4'-11 1/2" · front 4'-11 1/2"
Guard 36" min above the deck; openings under 4" (IRC R312). Rail LF for labor = deck-edge LF of actual rail.

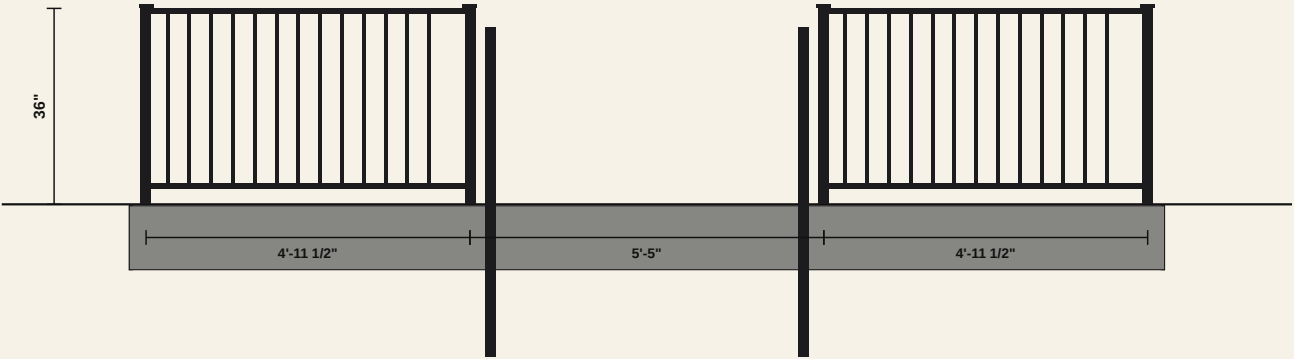

Plan above · elevation of the outer edge below

Design intent per 2021 IRC R507 prescriptive. Field verify. Do not scale.

16 x 14 deck · A-301 · Section + front elevation


A-301

SECTION + FRONT ELEVATION


Cut through the deepest zone; heights to grade, frost line, cantilever, guard

16 x 14 Deck — TimberTech Prime+ Sea Salt Gray, Fulton rail

GSX · Jade Pender 303-550-9558 · September 30, 2026 · Rev 0 · PERMIT SET

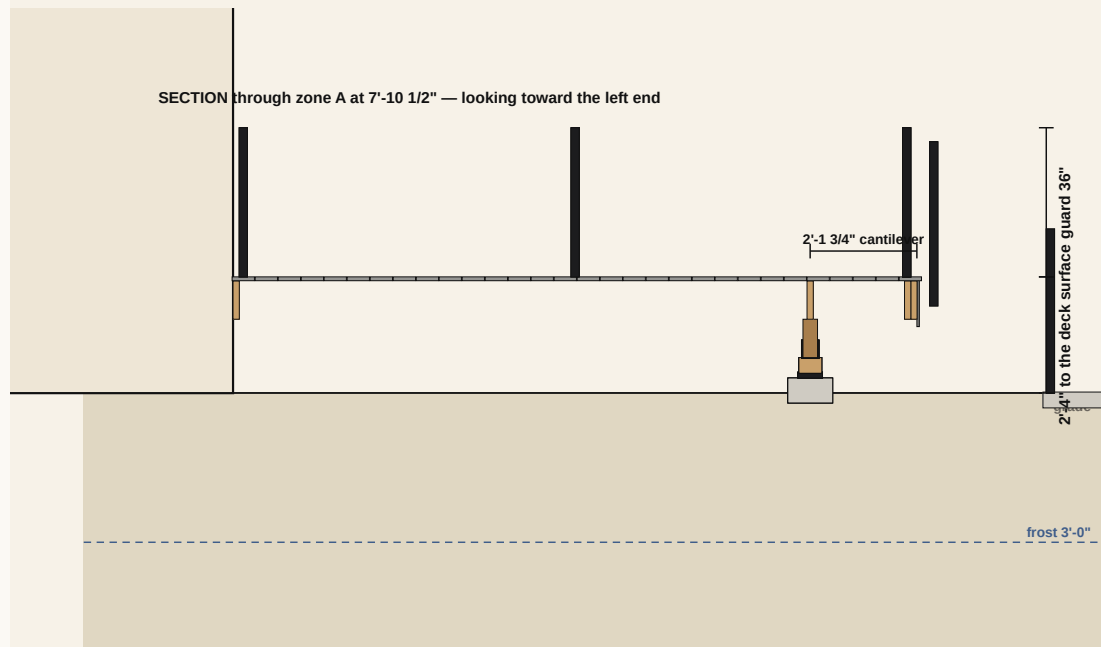

FRONT ELEVATION — from the yard

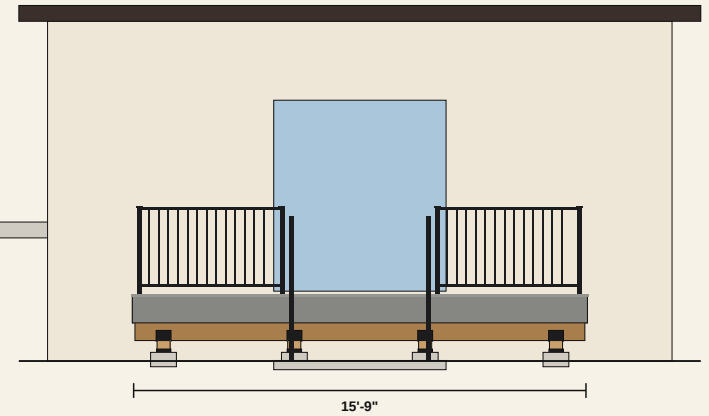

SECTION NOTES

Deck surface 2'-4" above grade; guard 36" where the drop exceeds 30"

DROP 4x10 DF: 15'-8"; 4 posts at 1'-0 1/2" / 5'-7 3/16" / 10'-1 13/16" / 14'-8 1/2" (worst 1,796 lb)

Posts 4 x 6x6 on DP-50/50

2x10 ledger x 15'-9" total · LedgerLOK 2 rows 2" from top/bottom, staggered 12" OC, first 3" from each end · 17 fasteners

G-Tape 2" every joist, PF joist, blocking and the ledger top · 4" on both rims and the beam(s)

Section left · elevation right · not to a common scale

Design intent per 2021 IRC R507 prescriptive. Field verify. Do not scale.

16 x 14 deck · D-501 · Details

D-501


DETAILS

Ledger · post / beam / cap · footing · rail post · deck edge · the job's special condition

16 x 14 Deck — TimberTech Prime+ Sea Salt Gray, Fulton rail


GSX · Jade Pender 303-550-9558 · September 30, 2026 · Rev 0 · PERMIT SET

1 LEDGER AT THE HOUSE

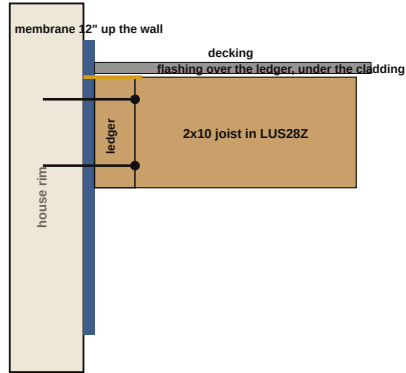


2x10 ledger x 15'-9" total · LedgerLOK 2 rows 2" from top/bottom, staggered 12" OC, first 3" from each end · 17 fasteners

2 POST · BEAM · CAP

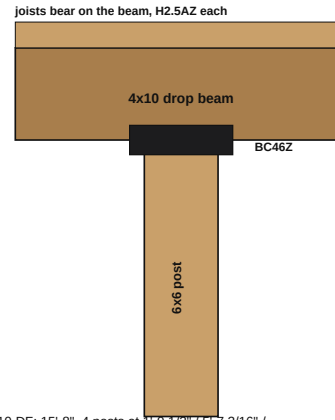


DROP 4x10 DF: 15'-8", 4 posts at 1'-0 1/2" / 7'-5" / 3'-16" / 10'-1 13/16" / 14'-8 1/2" (worst 1,796 lb)

3 FOOTING · POST BASE

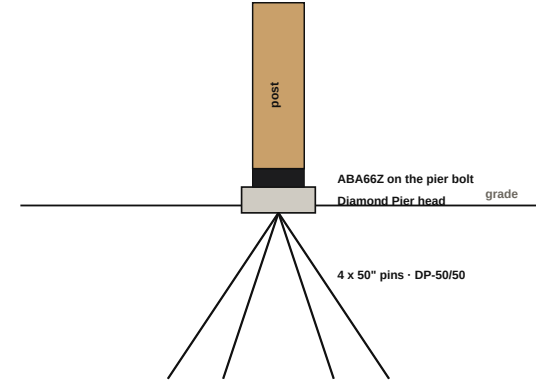


4 RAIL POST · GUARD

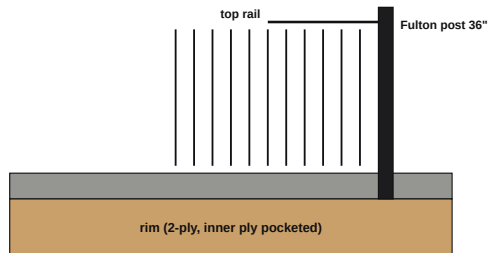

Fulton 36" — 8 posts (2 CORNER, 4 END, 2 LINE) inside the outer rim ply, inner ply pocketed 2" wide, (2) 7/16" x 4-1/2" bolts per post

5 DECK EDGE · BORDER

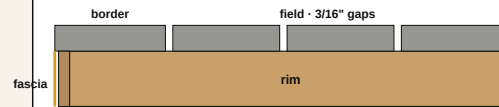

overhang 1 1/16"

100% hidden — Camo EdgeClip 3/16" at every joist in every gap (13 bearing points x 29 gaps = 377); board ends clipped on the PF joists, never screwed

6 BLOCKING

Blocking one row over the beam, staggered up and down so every block can be end-nailed.

Schematic details, not to scale

Design intent per 2021 IRC R507 prescriptive. Field verify. Do not scale.

16 x 14 deck



From the yard



From the front corner



Isometric



Under the deck

